Схема монтажа кабельных лотков структурированной кабельной системы
Административное здание (Здание В2), 1-й этаж

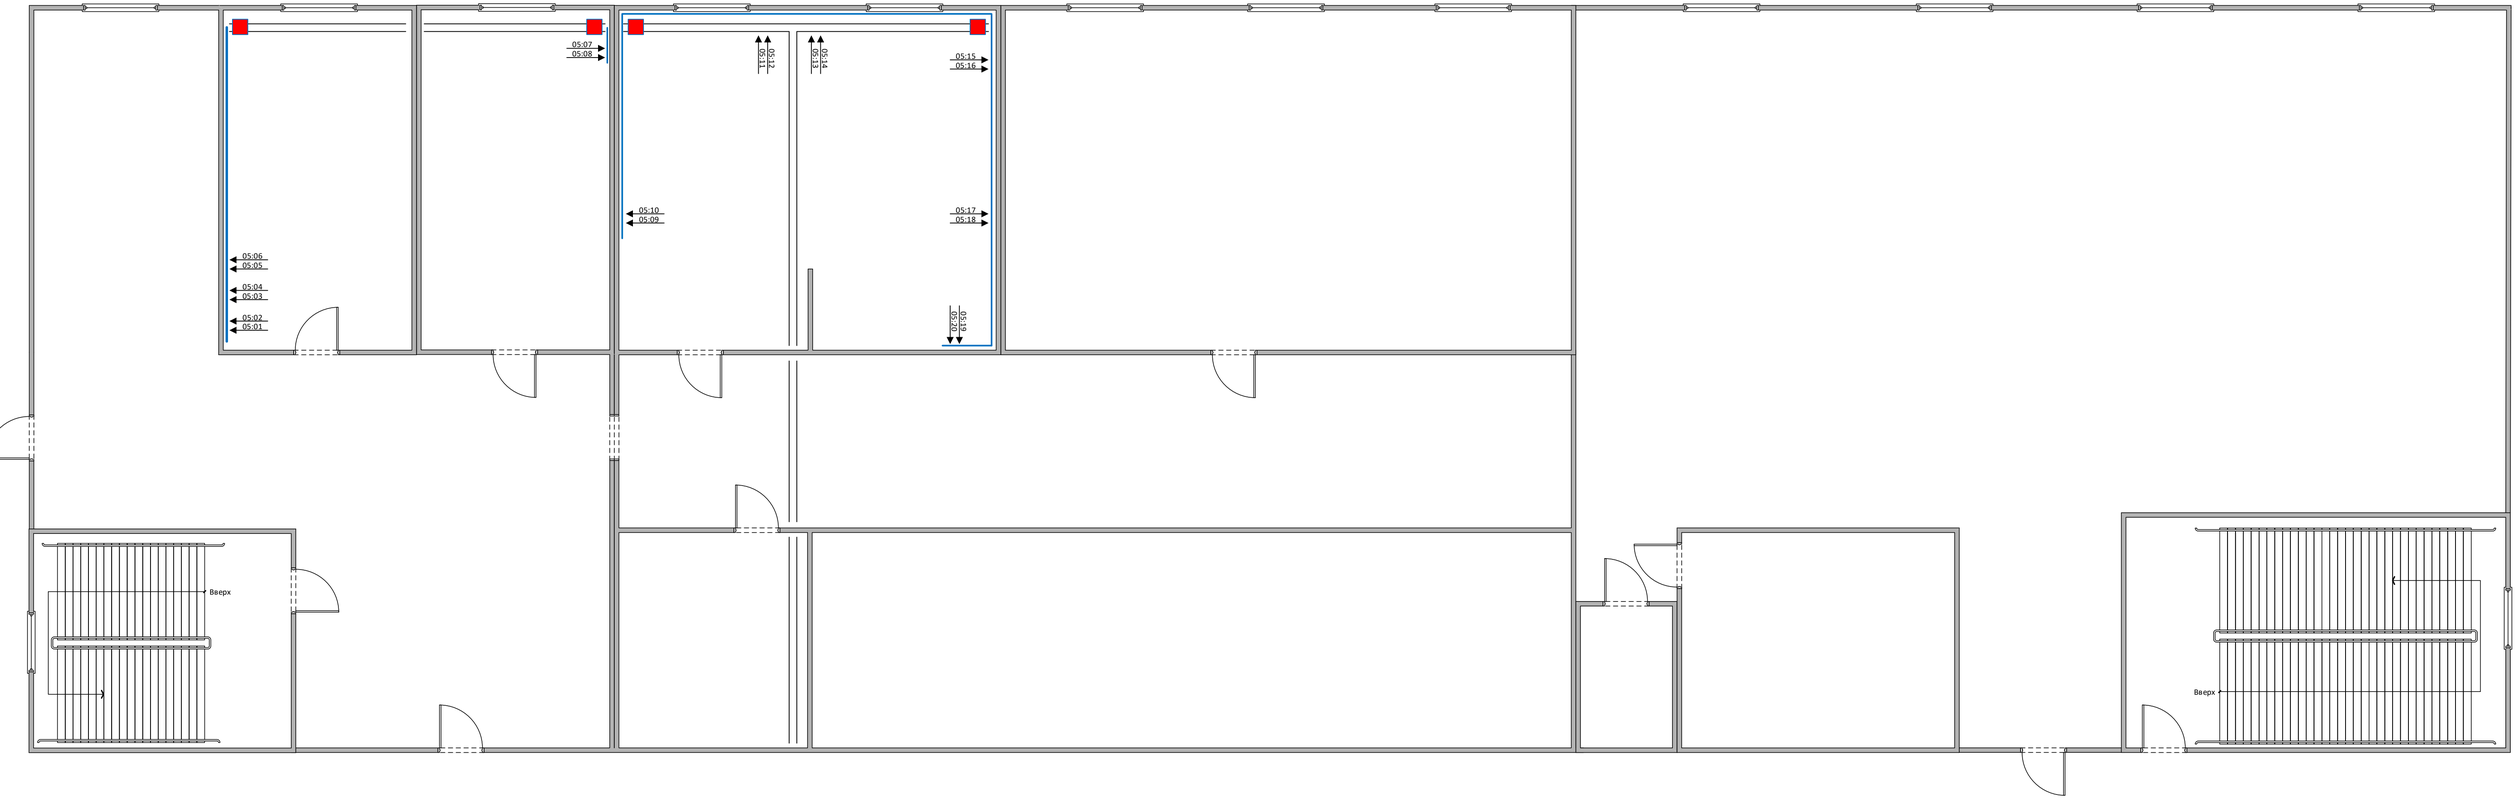


Схема монтажа кабельных лотков структурированной кабельной системы
Административный корпус (Здание В2), 2-й этаж


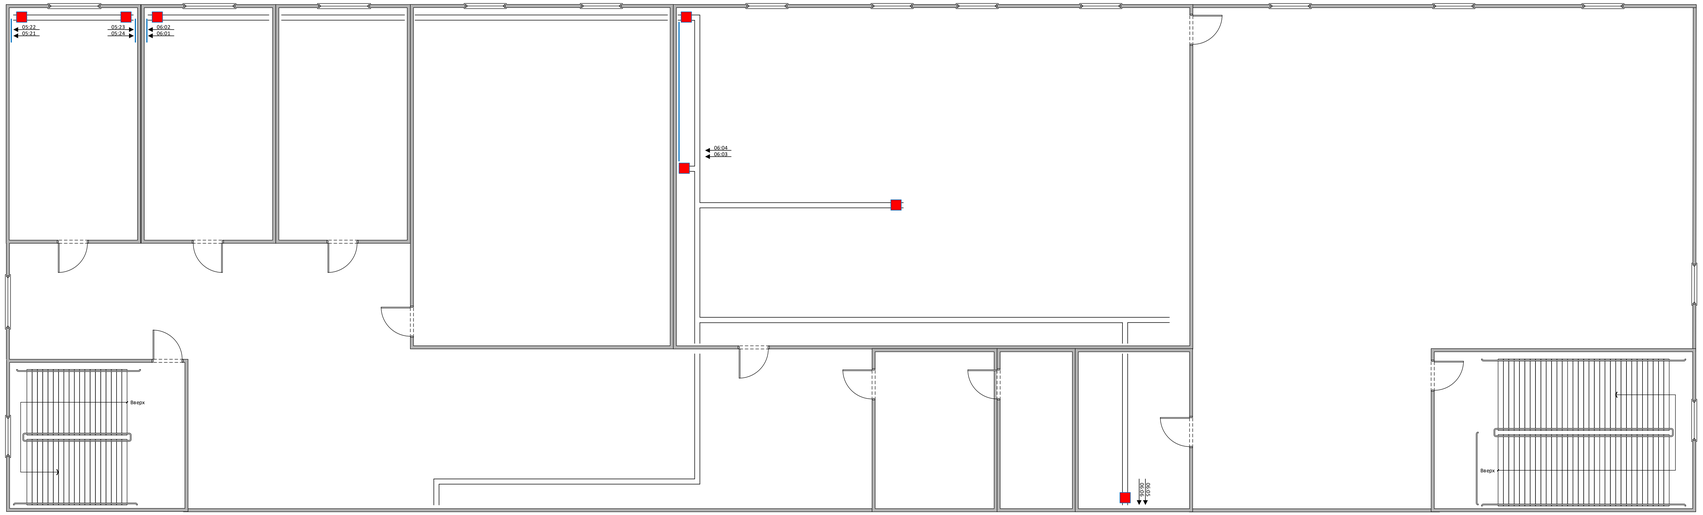


Схема монтажа кабельных лотков структурированной кабельной системы
Административный корпус (Здание В2), 3-й этаж

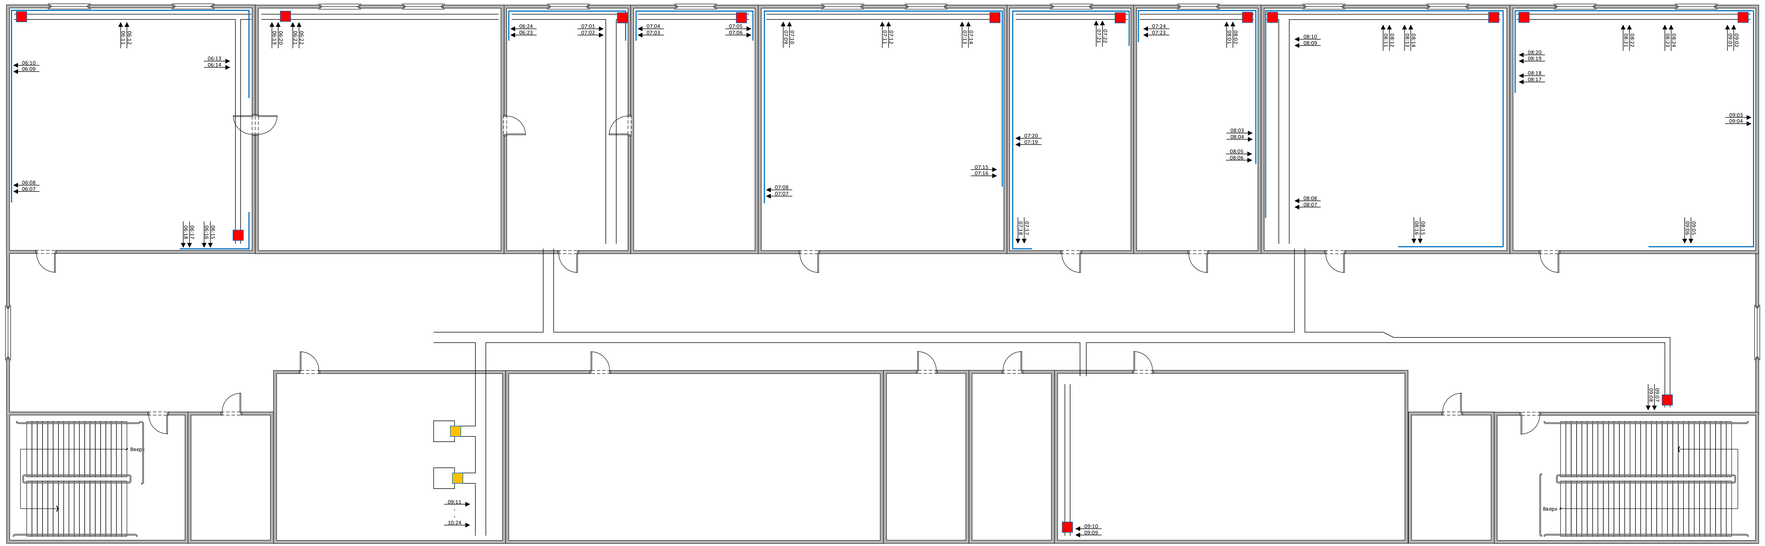

Проволочный лоток 50x200 мм

Проволочный лоток 50x100 мм

Миниканал кабельный 50x20 мм

Спуск в телекоммуникационный шкаф

Спуск в кабельканал с потолка

06.24 / 06.23 — Маркировка розеток рабочего места

Телекоммуникационный шкаф